
PROJECT MODUNEST - CORPORATE OFFICE DESIGN
109 BROCK ST. BARRIE, ONTARIO L4N 2N3
INDE 3001 - INTERIOR DETAILING 3

DESIGNED BY: TAYLOR GILES
DESIGNED FOR: FARIBA MOLKI

LIST OF DRAWINGS		
SHEET NUMBER	SHEET NAME	SCALE
ID	COVER SHEET	NOT APPLICABLE
ID-0	SITE PLAN	1/16" = 1'-0"
ID-1	EXISTING PLAN	1/8" = 1'-0"
ID-1.1	PARTITION PLAN	1/8" = 1'-0"
ID-1.2	FURNITURE PLAN	1/8" = 1'-0"
ID-1.3	REFLECTED CEILING PLAN	1/8" = 1'-0"
ID-1.4	POWER AND COMMUNICATION PLAN	1/8" = 1'-0"
ID-2	INTERIOR ELEVATIONS AND SECTION	1/8" = 1'-0"
ID-3	WALL DETAILS	1/4" = 1'-0"
ID-4	DOOR AND WINDOW SCHEDULE	1/4" = 1'-0"

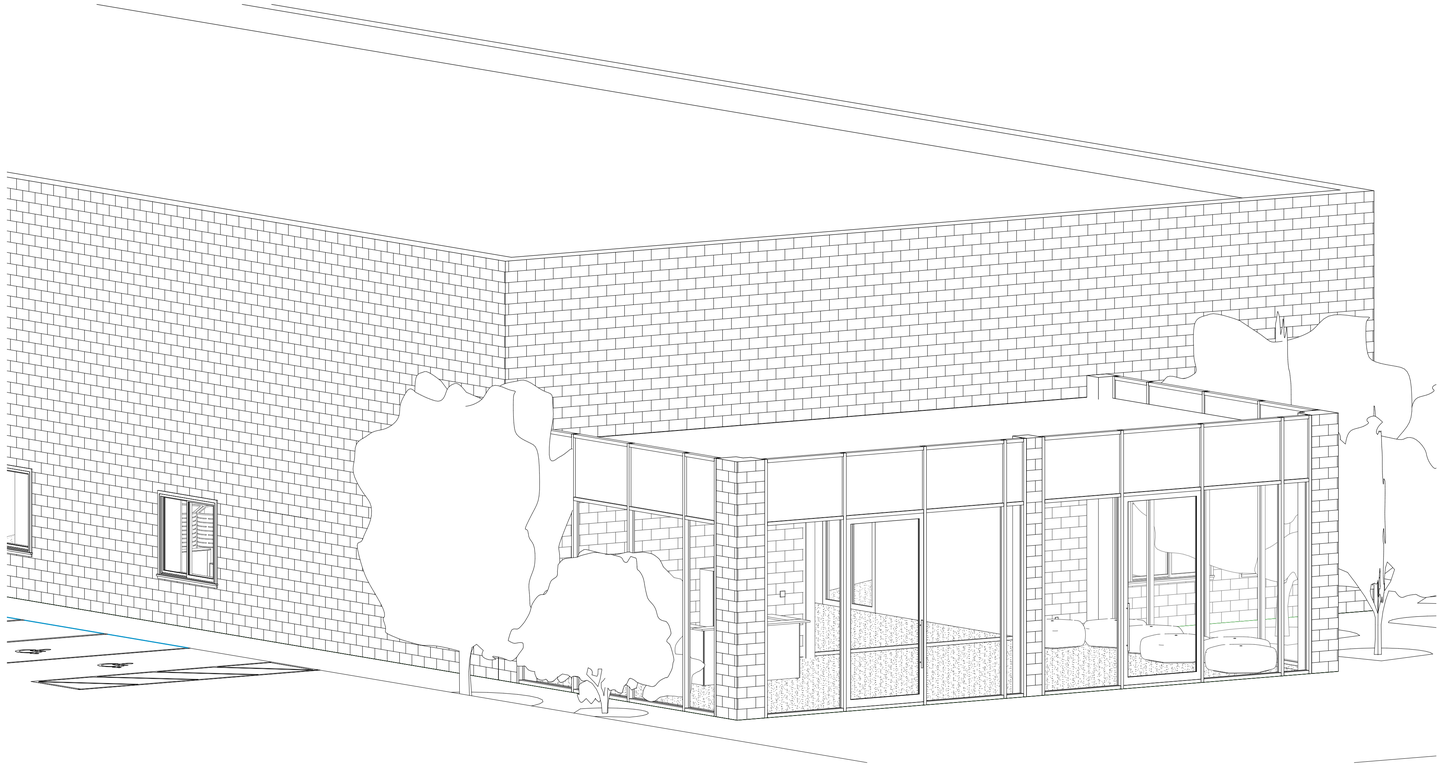

TAYLOR DESIGNS

GILES.TAYLOR@YAHOO.COM - (705) 826-4206
1 GEORGIAN DR. BARRIE, ON

GENERAL NOTES:

1. THE CONTRACTOR AND ALL SUB-CONTRACTORS SHALL VERIFY ALL DIMENSIONS, DETAILS AND SPECIFICATIONS ON SITE AND REPORT ALL DISCREPANCIES IN WRITING TO THE DESIGNER BEFORE PROCEEDING WITH THE WORK.
2. DRAWINGS ARE NOT TO BE SCALED.
3. THE CONTRACTOR AND SUB-CONTRACTORS, BEFORE PROCEEDING WITH THE WORK, MUST SUBMIT ALL NECESSARY SAMPLES AND SHOP DRAWINGS TO THE DESIGNER FOR APPROVAL.
4. ALL CONCEPTS, DESIGNS, DETAILS, DRAWINGS AND SPECIFICATIONS ARE STUDENT WORK, AND THE PROPERTY OF THE DESIGNER. AS SUCH, THEY ARE NOT INTENDED FOR USE ON OTHER PROJECTS OR EXTENSIONS OF THE SPECIFIED PROJECT WHATSOEVER.

OWNERSHIP: ALL DRAWINGS, SPECIFICATIONS, DESIGNS & COPIES THEROF ARE THE PROPERTY OF THE DESIGNER AND THE OWNER, WHETHER OR NOT THE WORK FOR WHICH THEY ARE MADE IS PERFORMED, AND ARE NOT TO BE USED OR DUPLICATED ON OTHER WORK EXCEPT BY WRITTEN CONSENT FROM THE DESIGNER AND OWNER.

REV	DESCRIPTION	DATE

PROJECT: PROJECT MODUNEST

DRAWING: COVER SHEET

DESIGNED BY: Taylor Giles

ISSUE DATE: 12/04/25


ADDRESS: 109 BROCK ST. BARRIE, ON L4N 2M3

SHEET: ID


COURSE: INDE3001

SCALE:

2025-12-03 11:40:17 PM

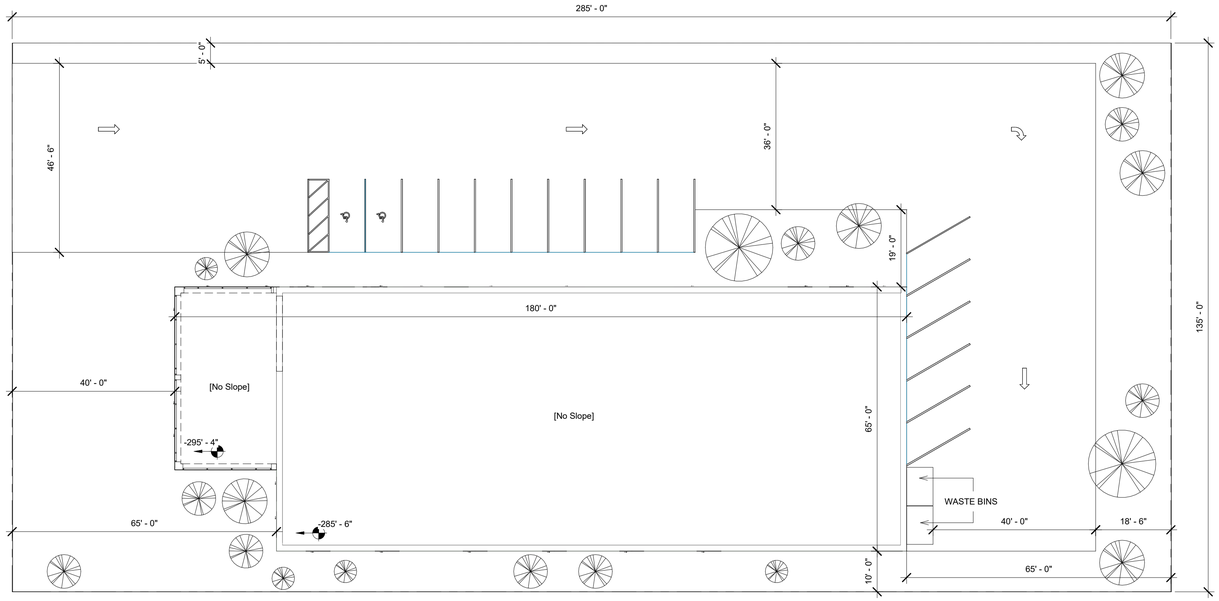

1 SITE PLAN
1/16" = 1'-0"

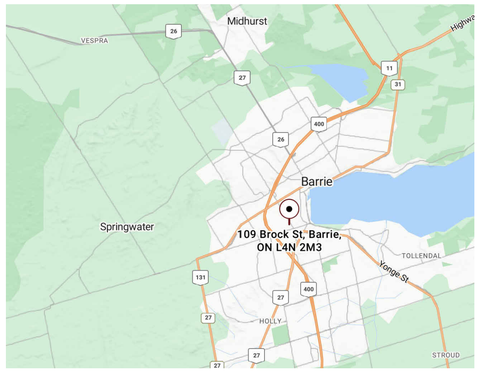

PROXIMITY MAP
1/4" = 1'-0"

SITE INFORMATION

PROJECT LOCATION: BARRIE, ONTARIO
ZONING: COMMERCIAL
LEGAL ADDRESS: 109 BROCK ST. BARRIE ON L4N 2M3
SITE AREA: 38, 475 SQ FT.
BUILDING FOOTPRINT: 11, 700 SQ FT.
REAR SET BACK: 65'
FRONT SET BACK: 40'
GRADE LEVEL: 310'

WASTE MANAGEMENT

THE WASTE MANAGEMENT PLAN FOR MODUNEST ENSURES ALL WASTE IS COLLECTED, SORTED, AND DISPOSED OF SAFELY AND EFFICIENTLY, WITH CENTRALIZED THREE-STREAM STATIONS (RECYCLING, ORGANICS, AND LANDFILL) PLACED THROUGHOUT THE OFFICE AND CLEAR SIGNAGE TO GUIDE STAFF. INTERIOR WASTE IS TRANSFERRED DAILY TO SECURED EXTERIOR BINS LOCATED AT THE REAR OF THE BUILDING, WHERE SCREENED, WELL-LIT, AND PEST-RESISTANT ENCLOSURES HOUSE DEDICATED DUMPSTERS FOR GENERAL WASTE, RECYCLING, AND ORGANICS. HAZARDOUS MATERIALS SUCH AS BATTERIES, TONER, AND E-WASTE ARE STORED SEPARATELY AND COLLECTED BY CERTIFIED VENDORS. THE WASTE HAULER SERVICES THE REAR ENCLOSURE ON A SCHEDULED BASIS — TYPICALLY ONCE OR TWICE PER WEEK—WHILE STAFF COMPLETE ROUTINE CLEANING AND MONITORING TO PREVENT CONTAMINATION, MAINTAIN HYGIENE, AND SUPPORT SUSTAINABILITY GOALS THROUGH REGULAR AUDITS AND PROPER WASTE DIVERSION PRACTICES.

TAYLOR DESIGNS

GILES.TAYLOR@YAHOO.COM - (705) 826-4206
1 GEORGIAN DR. BARRIE, ON

GENERAL NOTES:

1. THE CONTRACTOR AND ALL SUB-CONTRACTORS SHALL VERIFY ALL DIMENSIONS, DETAILS AND SPECIFICATIONS ON SITE AND REPORT ALL DISCREPANCIES IN WRITING TO THE DESIGNER BEFORE PROCEEDING WITH THE WORK.
2. DRAWINGS ARE NOT TO BE SCALED.
3. THE CONTRACTOR AND SUB-CONTRACTORS, BEFORE PROCEEDING WITH THE WORK, MUST SUBMIT ALL NECESSARY SAMPLES AND SHOP DRAWINGS TO THE DESIGNER FOR APPROVAL.
4. ALL CONCEPTS, DESIGNS, DETAILS, DRAWINGS AND SPECIFICATIONS ARE STUDENT WORK AND THE PROPERTY OF THE DESIGNER. AS SUCH, THEY ARE NOT INTENDED FOR USE ON OTHER PROJECTS OR EXTENSIONS OF THE SPECIFIED PROJECT WHATSOEVER.

OWNERSHIP: ALL DRAWINGS, SPECIFICATIONS, DESIGNS & COPIES THEROF ARE THE PROPERTY OF THE DESIGNER AND THE OWNER, WHETHER OR NOT THE WORK FOR WHICH THEY ARE MADE IS PERFORMED, AND ARE NOT TO BE USED OR DUPLICATED ON OTHER WORK EXCEPT BY WRITTEN CONSENT FROM THE DESIGNER AND OWNER.

REV	DESCRIPTION	DATE

PROJECT: PROJECT MODUNEST

ADDRESS: 109 BROCK ST. BARRIE, ON L4N 2M3

DRAWING: SITE PLAN

SHEET: ID-0


DESIGNED BY: Taylor Giles

ISSUE DATE: 12/04/25

COURSE: INDE3001

SCALE: As indicated

2025-12-03 11:40:18 PM

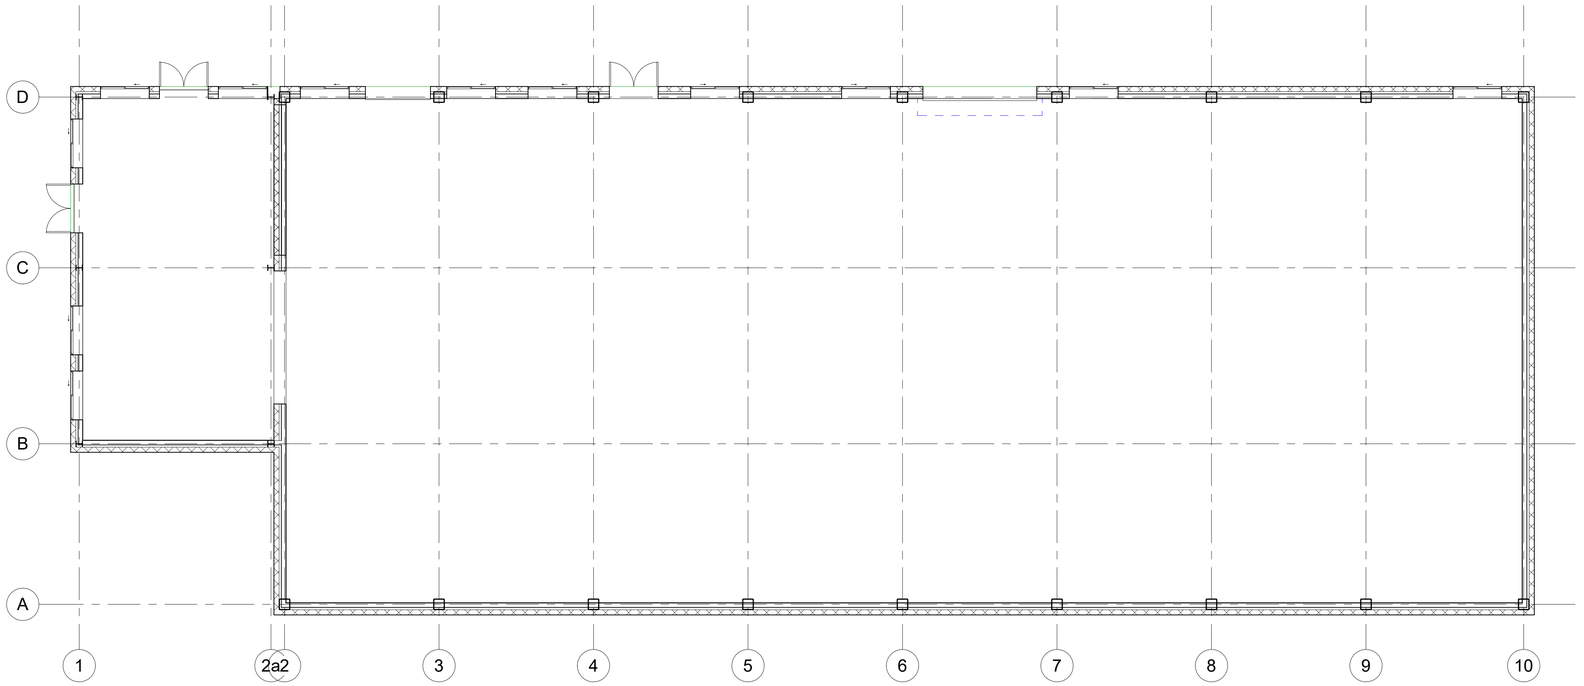

1 EXISTING PLAN
1/8" = 1'-0"

TAYLOR DESIGNS

GILES.TAYLOR@YAHOO.COM - (705) 826-4206
1 GEORGIAN DR. BARRIE, ON

GENERAL NOTES:

1. THE CONTRACTOR AND ALL SUB-CONTRACTORS SHALL VERIFY ALL DIMENSIONS, DETAILS AND SPECIFICATIONS ON SITE AND REPORT ALL DISCREPANCIES IN WRITING TO THE DESIGNER BEFORE PROCEEDING WITH THE WORK.
2. DRAWINGS ARE NOT TO BE SCALED.
3. THE CONTRACTOR AND SUB-CONTRACTORS, BEFORE PROCEEDING WITH THE WORK, MUST SUBMIT ALL NECESSARY SAMPLES AND SHOP DRAWINGS TO THE DESIGNER FOR APPROVAL.
4. ALL CONCEPTS, DESIGNS, DETAILS, DRAWINGS AND SPECIFICATIONS ARE STUDENT WORK AND THE PROPERTY OF THE DESIGNER. AS SUCH, THEY ARE NOT INTENDED FOR USE ON OTHER PROJECTS OR EXTENSIONS OF THE SPECIFIED PROJECT WHATSOEVER.

OWNERSHIP: ALL DRAWINGS, SPECIFICATIONS, DESIGNS & COPIES THEROF ARE THE PROPERTY OF THE DESIGNER AND THE OWNER, WHETHER OR NOT THE WORK FOR WHICH THEY ARE MADE IS PERFORMED, AND ARE NOT TO BE USED OR DUPLICATED ON OTHER WORK EXCEPT BY WRITTEN CONSENT FROM THE DESIGNER AND OWNER.

REV	DESCRIPTION	DATE

PROJECT: PROJECT MODUNEST

ADDRESS: 109 BROCK ST. BARRIE, ON L4N 2M3

DRAWING: EXISTING PLAN

SHEET: ID-1


DESIGNED BY: Taylor Giles

ISSUE DATE: 12/04/25

COURSE: INDE3001

SCALE: 1/8" = 1'-0"

2025-12-03 11:40:18 PM

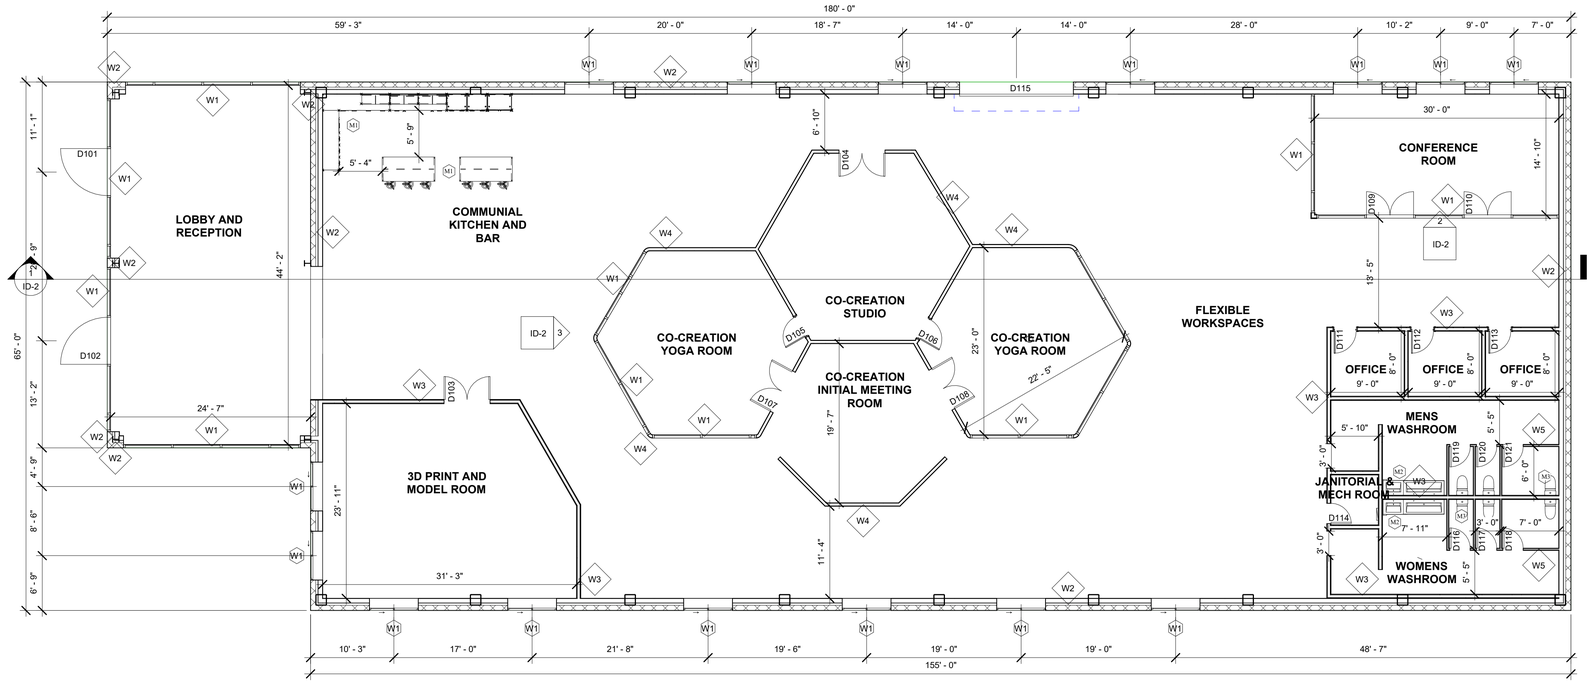

1 PARTITION PLAN
1/8" = 1'-0"

MILWORK AND CASEMENT SCHEDULE

TAG	DESCRIPTION	MANUFACTURER	COUNT
M1	COMMUNITY KITCHEN	TEKNION	1
M2	ADA VANITY	SLOAN	2
M3	ADA WALL MOUNTED TOLIET	SLOAN	6

MILWORK AND CASEMENT SCHEDULE
1/4" = 1'-0"

TAYLOR DESIGNS

GILES.TAYLOR@YAHOO.COM - (705) 826-4206
1 GEORGIAN DR. BARRIE, ON

GENERAL NOTES:

1. THE CONTRACTOR AND ALL SUB-CONTRACTORS SHALL VERIFY ALL DIMENSIONS, DETAILS AND SPECIFICATIONS ON SITE AND REPORT ALL DISCREPANCIES IN WRITING TO THE DESIGNER BEFORE PROCEEDING WITH THE WORK.
2. DRAWINGS ARE NOT TO BE SCALED.
3. THE CONTRACTOR AND SUB-CONTRACTORS, BEFORE PROCEEDING WITH THE WORK, MUST SUBMIT ALL NECESSARY SAMPLES AND SHOP DRAWINGS TO THE DESIGNER FOR APPROVAL.
4. ALL CONCEPTS, DESIGNS, DETAILS, DRAWINGS AND SPECIFICATIONS ARE STUDENT WORK AND THE PROPERTY OF THE DESIGNER. AS SUCH, THEY ARE NOT INTENDED FOR USE ON OTHER PROJECTS OR EXTENSIONS OF THE SPECIFIED PROJECT WHATSOEVER.

OWNERSHIP: ALL DRAWINGS, SPECIFICATIONS, DESIGNS & COPIES THEROF ARE THE PROPERTY OF THE DESIGNER AND THE OWNER, WHETHER OR NOT THE WORK FOR WHICH THEY ARE MADE IS PERFORMED, AND ARE NOT TO BE USED OR DUPLICATED ON OTHER WORK EXCEPT BY WRITTEN CONSENT FROM THE DESIGNER AND OWNER.

REV	DESCRIPTION	DATE

PROJECT: PROJECT MODUNEST

ADDRESS: 109 BROCK ST. BARRIE, ON L4N 2M3

DRAWING: PARTITION PLAN

SHEET: ID-1.1


DESIGNED BY: Taylor Giles

ISSUE DATE: 12/04/25

COURSE: INDE3001

SCALE: As indicated

2025-12-03 11:40:19 PM

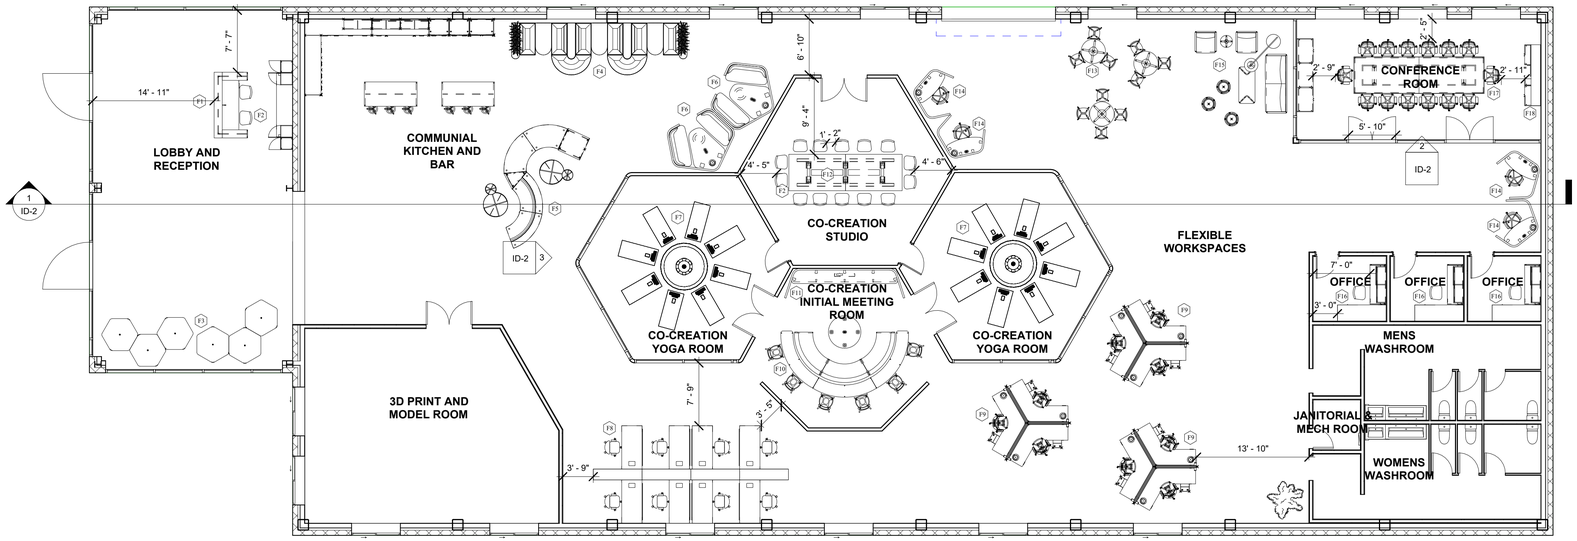

1 FURNITURE PLAN
1/8" = 1'-0"

FURNITURE SCHEDULE			
TAG	DESCRIPTION	MANUFACTURER	QTY
F1	RECEPTION CASEGOODS	TEKNION	1
F2	OFFICE CHAIR	TEKNION	16
F3	MODULAR HEXIGONAL SEATING	TEKNION	6
F4	BANQUETTE SEATING	TEKNION	2
F5	MODULAR SOFA AND TABLES	TEKNION	1
F6	LOUNGE MEETING POD	TEKNION	2
F7	YOGA MATS AND FOUNTAIN	TEKNION	2
F8	UPSTAGE WORKSPACES	TEKNION	1
F9	HEIGHT ADJUSTABLE WORKSPACE	TEKNION	3
F10	ZONES MODULAR SEATING	TEKNION	1
F11	TV PROJECTION CONSOLE	TEKNION	1
F12	HEIGHT ADJUSTABLE MEETING TABLE	TEKNION	1
F13	MODULAR ROUND TABLE AND CHAIRS	TEKNION	3
F14	FOCUS ZONE PODS	TEKNION	4
F15	LOUNGE SOFA AND CHAIRS	TEKNION	1
F16	PRIVATE OFFICE FURNITURE	TEKNION	3
F17	CONFERENCE TABLE AND CHAIRS	TEKNION	1
F18	STORAGE CONSOLE	TEKNION	2

TAYLOR DESIGNS

GILES.TAYLOR@YAHOO.COM - (705) 826-4206
1 GEORGIAN DR. BARRIE, ON

GENERAL NOTES:

1. THE CONTRACTOR AND ALL SUB-CONTRACTORS SHALL VERIFY ALL DIMENSIONS, DETAILS AND SPECIFICATIONS ON SITE AND REPORT ALL DISCREPANCIES IN WRITING TO THE DESIGNER BEFORE PROCEEDING WITH THE WORK.
2. DRAWINGS ARE NOT TO BE SCALED.
3. THE CONTRACTOR AND SUB-CONTRACTORS, BEFORE PROCEEDING WITH THE WORK, MUST SUBMIT ALL NECESSARY SAMPLES AND SHOP DRAWINGS TO THE DESIGNER FOR APPROVAL.
4. ALL CONCEPTS, DESIGNS, DETAILS, DRAWINGS AND SPECIFICATIONS ARE STUDENT WORK AND THE PROPERTY OF THE DESIGNER. AS SUCH, THEY ARE NOT INTENDED FOR USE ON OTHER PROJECTS OR EXTENSIONS OF THE SPECIFIED PROJECT WHATSOEVER.

OWNERSHIP: ALL DRAWINGS, SPECIFICATIONS, DESIGNS & COPIES THEROF ARE THE PROPERTY OF THE DESIGNER AND THE OWNER, WHETHER OR NOT THE WORK FOR WHICH THEY ARE MADE IS PERFORMED, AND ARE NOT TO BE USED OR DUPLICATED ON OTHER WORK EXCEPT BY WRITTEN CONSENT FROM THE DESIGNER AND OWNER.

REV	DESCRIPTION	DATE

PROJECT: PROJECT MODUNEST

ADDRESS: 109 BROCK ST. BARRIE, ON L4N 2M3

DRAWING: FURNITURE PLAN

SHEET: ID-1.2


DESIGNED BY: Taylor Giles

ISSUE DATE: 12/04/25

COURSE: INDE3001

SCALE: 1/8" = 1'-0"

2025-12-03 11:40:21 PM

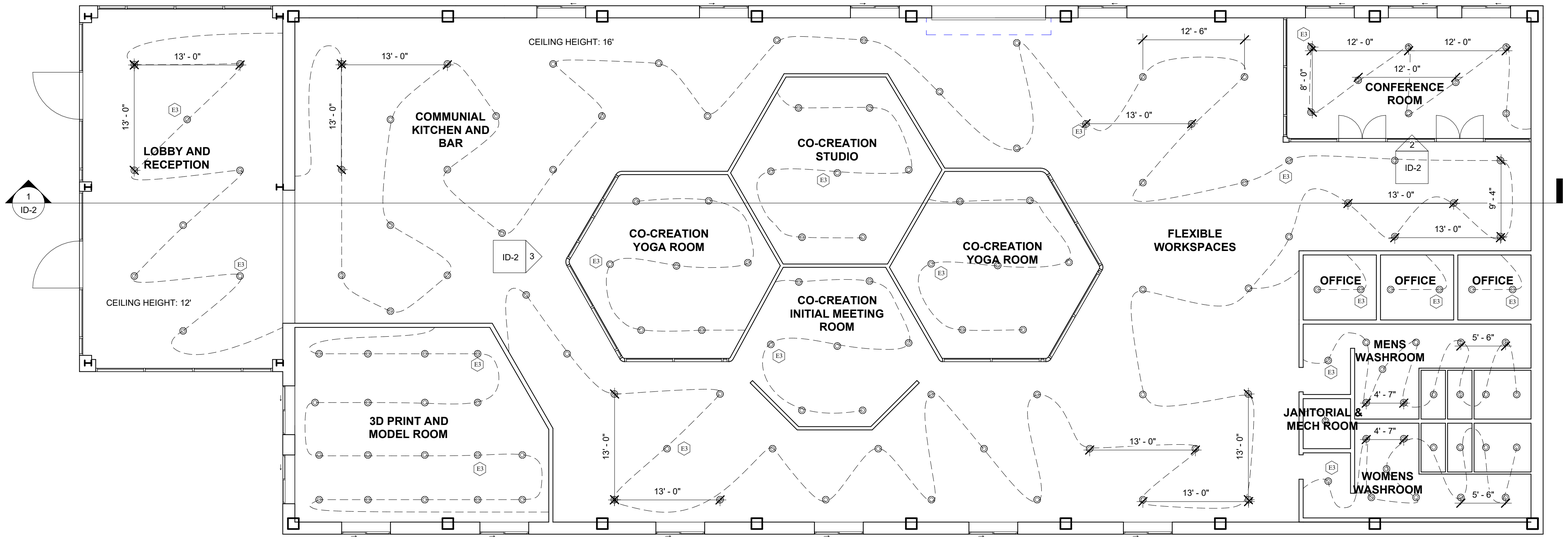

1 REFLECTED CEILING PLAN
1/8" = 1'-0"

ALL CEILING HEIGHTS ARE 16' EXCEPT THE LOBBY AND RECEPTION IS 12'.
ALL CEILINGS ARE GYPSUM BOARD

SYMBOL LEGEND

SYMBOL	USAGE
◎	CEILING RECESSED LIGHT
- - - -	WIRING

SYMBOL LEGEND FOR LIGHTING
1/4" = 1'-0"

TAYLOR DESIGNS

GILES.TAYLOR@YAHOO.COM - (705) 826-4206
1 GEORGIAN DR. BARRIE, ON

GENERAL NOTES:

1. THE CONTRACTOR AND ALL SUB-CONTRACTORS SHALL VERIFY ALL DIMENSIONS, DETAILS AND SPECIFICATIONS ON SITE AND REPORT ALL DISCREPANCIES IN WRITING TO THE DESIGNER BEFORE PROCEEDING WITH THE WORK.
2. DRAWINGS ARE NOT TO BE SCALED.
3. THE CONTRACTOR AND SUB-CONTRACTORS, BEFORE PROCEEDING WITH THE WORK, MUST SUBMIT ALL NECESSARY SAMPLES AND SHOP DRAWINGS TO THE DESIGNER FOR APPROVAL.
4. ALL CONCEPTS, DESIGNS, DETAILS, DRAWINGS AND SPECIFICATIONS ARE STUDENT WORK AND THE PROPERTY OF THE DESIGNER. AS SUCH, THEY ARE NOT INTENDED FOR USE ON OTHER PROJECTS OR EXTENSIONS OF THE SPECIFIED PROJECT WHATSOEVER.

OWNERSHIP: ALL DRAWINGS, SPECIFICATIONS, DESIGNS & COPIES THEROF ARE THE PROPERTY OF THE DESIGNER AND THE OWNER, WHETHER OR NOT THE WORK FOR WHICH THEY ARE MADE IS PERFORMED, AND ARE NOT TO BE USED OR DUPLICATED ON OTHER WORK EXCEPT BY WRITTEN CONSENT FROM THE DESIGNER AND OWNER.

REV.	DESCRIPTION	DATE

PROJECT: PROJECT MODUNEST

ADDRESS: 109 BROCK ST. BARRIE, ON L4N 2M3

DRAWING: REFLECTED CEILING PLAN

SHEET: ID-1.3


DESIGNED BY: Taylor Giles

ISSUE DATE: 12/04/25

COURSE: INDE3001

SCALE: As indicated

2025-12-03 11:40:21 PM

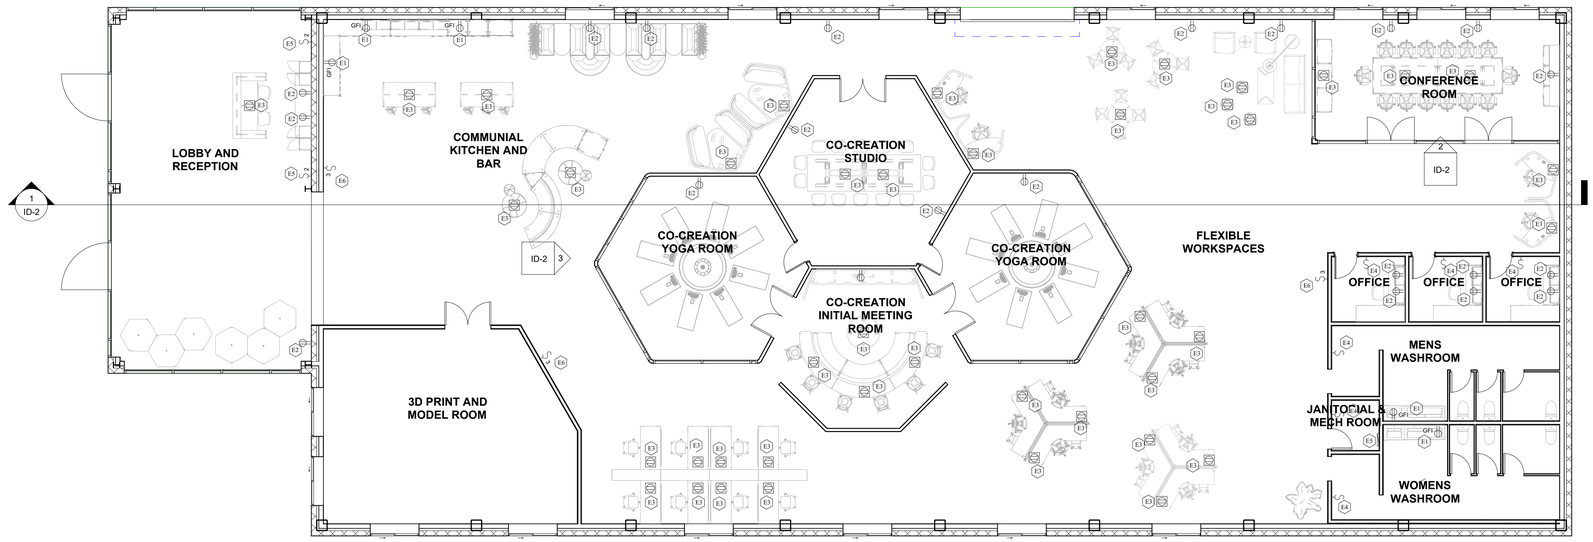

1 POWER AND COMMUNICATION PLAN
1/8" = 1'-0"

ELECTRICAL AND COMMUNICATION SCHEDULE			
TAG	TYPE	MANUFACTURER	VOLTAGE
E1	OUTLET-GFI: SINGLE	LEVITON	125 VOLT
E2	OUTLET-DUPLEX: SINGLE	LEVITON	125 VOLT
E3	OUTLET FLOOR-DUPLEX: SINGLE	LEVITON	125 VOLT
E4	SWITCH-SINGLE: SINGLE	LEVITON	15 VOLT
E5	SWITCH-DOUBLE: DOUBLE	LEVITON	15 VOLT
E6	SWITCH-THREE WAY: THREE WAY	LEVITON	15 VOLT

GRAND TOTAL: 81

SYMBOL LEGEND

SYMBOL	USAGE
GFI	GFI OUTLET
	SINGLE DUPLEX OUTLET
	FLOOR OUTLET
	ELECTRICAL PANEL
S	SINGLE SWITCH
S2	DOUBLE SWITCH
S3	THREE WAY SWITCH

SYMBOL LEGEND
1/4" = 1'-0"

TAYLOR DESIGNS

GILES.TAYLOR@YAHOO.COM - (705) 826-4206
1 GEORGIAN DR. BARRIE, ON

GENERAL NOTES:

1. THE CONTRACTOR AND ALL SUB-CONTRACTORS SHALL VERIFY ALL DIMENSIONS, DETAILS AND SPECIFICATIONS ON SITE AND REPORT ALL DISCREPANCIES IN WRITING TO THE DESIGNER BEFORE PROCEEDING WITH THE WORK.
2. DRAWINGS ARE NOT TO BE SCALED.
3. THE CONTRACTOR AND SUB-CONTRACTORS, BEFORE PROCEEDING WITH THE WORK, MUST SUBMIT ALL NECESSARY SAMPLES AND SHOP DRAWINGS TO THE DESIGNER FOR APPROVAL.
4. ALL CONCEPTS, DESIGNS, DETAILS, DRAWINGS AND SPECIFICATIONS ARE STUDENT WORK AND THE PROPERTY OF THE DESIGNER. AS SUCH, THEY ARE NOT INTENDED FOR USE ON OTHER PROJECTS OR EXTENSIONS OF THE SPECIFIED PROJECT WHATSOEVER.

OWNERSHIP: ALL DRAWINGS, SPECIFICATIONS, DESIGNS & COPIES THEROF ARE THE PROPERTY OF THE DESIGNER AND THE OWNER, WHETHER OR NOT THE WORK FOR WHICH THEY ARE MADE IS PERFORMED, AND ARE NOT TO BE USED OR DUPLICATED ON OTHER WORK EXCEPT BY WRITTEN CONSENT FROM THE DESIGNER AND OWNER.

REV	DESCRIPTION	DATE

PROJECT: PROJECT MODUNEST

ADDRESS: 109 BROCK ST. BARRIE, ON L4N 2M3

DRAWING: POWER AND COMMUNICATION PLAN

SHEET: ID-1.4


DESIGNED BY: Taylor Giles

ISSUE DATE: 12/04/25


COURSE: INDE3001

SCALE: As indicated


2025-12-03 11:40:24 PM

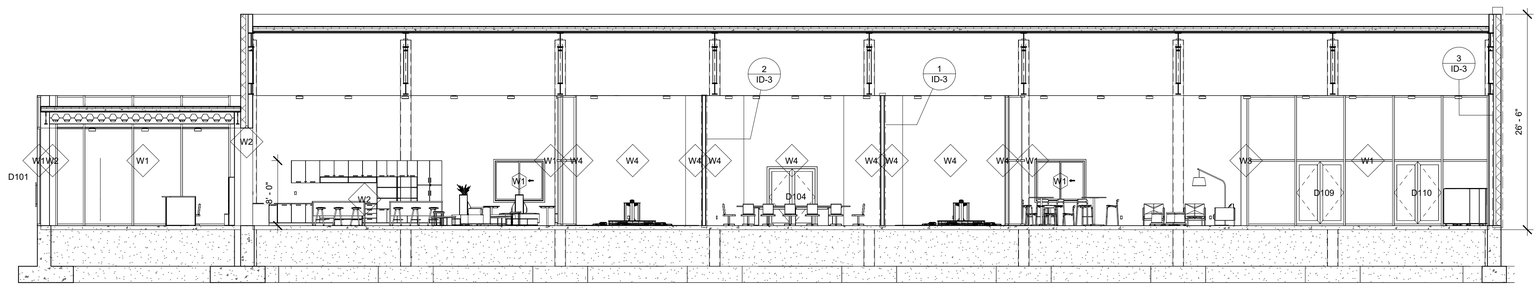

1 INTERIOR SECTION
1/8" = 1'-0"

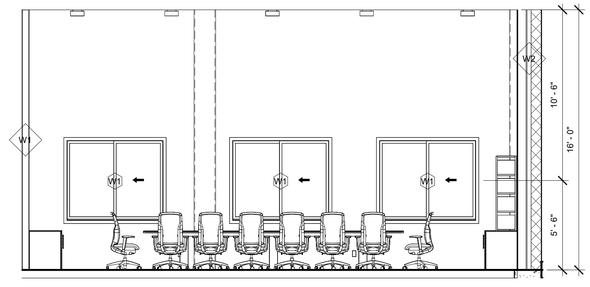

2 CONFERENCE ROOM ELEVATION
1/4" = 1'-0"

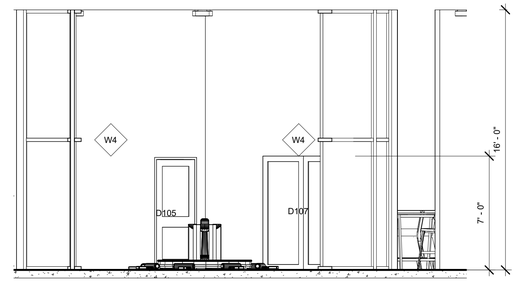

3 CO-CREATION SPACE ELEVATION
1/4" = 1'-0"

TAYLOR DESIGNS

GILES.TAYLOR@YAHOO.COM - (705) 826-4206
1 GEORGIAN DR. BARRIE, ON

GENERAL NOTES:

1. THE CONTRACTOR AND ALL SUB-CONTRACTORS SHALL VERIFY ALL DIMENSIONS, DETAILS AND SPECIFICATIONS ON SITE AND REPORT ALL DISCREPANCIES IN WRITING TO THE DESIGNER BEFORE PROCEEDING WITH THE WORK.
2. DRAWINGS ARE NOT TO BE SCALED.
3. THE CONTRACTOR AND SUB-CONTRACTORS, BEFORE PROCEEDING WITH THE WORK, MUST SUBMIT ALL NECESSARY SAMPLES AND SHOP DRAWINGS TO THE DESIGNER FOR APPROVAL.
4. ALL CONCEPTS, DESIGNS, DETAILS, DRAWINGS AND SPECIFICATIONS ARE STUDENT WORK AND THE PROPERTY OF THE DESIGNER. AS SUCH, THEY ARE NOT INTENDED FOR USE ON OTHER PROJECTS OR EXTENSIONS OF THE SPECIFIED PROJECT WHATSOEVER.

OWNERSHIP: ALL DRAWINGS, SPECIFICATIONS, DESIGNS & COPIES THEROF ARE THE PROPERTY OF THE DESIGNER AND THE OWNER, WHETHER OR NOT THE WORK FOR WHICH THEY ARE MADE IS PERFORMED, AND ARE NOT TO BE USED OR DUPLICATED ON OTHER WORK EXCEPT BY WRITTEN CONSENT FROM THE DESIGNER AND OWNER.

REV	DESCRIPTION	DATE

PROJECT:
PROJECT MODUNEST

ADDRESS:
109 BROCK ST. BARRIE, ON L4N 2M3

DRAWING:
INTERIOR ELEVATIONS AND SECTION

SHEET:
ID-2


DESIGNED BY: Taylor Giles

ISSUE DATE: 12/04/25


COURSE: INDE3001

SCALE: As indicated


2025-12-03 11:40:28 PM

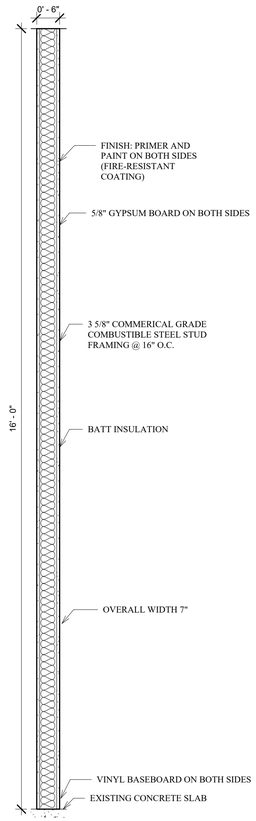

1 FIRE RATED (1HR)
3/4" = 1'-0"

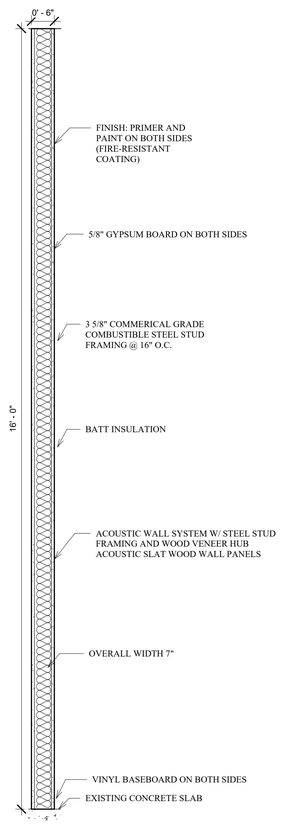

2 ACOUSTIC WALL
3/4" = 1'-0"

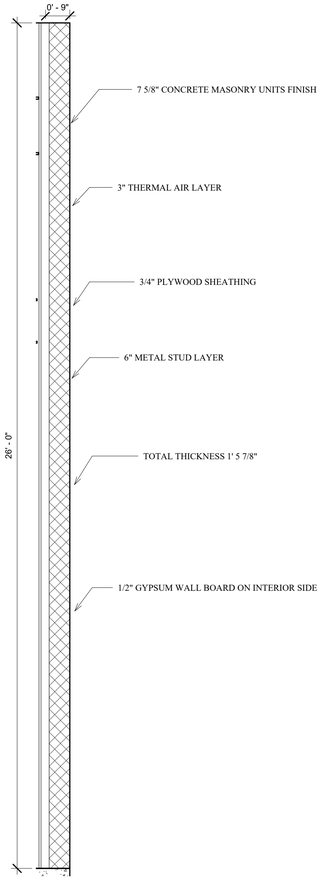

3 EXTERIOR WALL - CMU ON MTL. STUD
1/2" = 1'-0"

TAYLOR DESIGNS

GILES.TAYLOR@YAHOO.COM - (705) 826-4206
1 GEORGIAN DR. BARRIE, ON

GENERAL NOTES:

1. THE CONTRACTOR AND ALL SUB-CONTRACTORS SHALL VERIFY ALL DIMENSIONS, DETAILS AND SPECIFICATIONS ON SITE AND REPORT ALL DISCREPANCIES IN WRITING TO THE DESIGNER BEFORE PROCEEDING WITH THE WORK.
2. DRAWINGS ARE NOT TO BE SCALED.
3. THE CONTRACTOR AND SUB-CONTRACTORS, BEFORE PROCEEDING WITH THE WORK, MUST SUBMIT ALL NECESSARY SAMPLES AND SHOP DRAWINGS TO THE DESIGNER FOR APPROVAL.
4. ALL CONCEPTS, DESIGNS, DETAILS, DRAWINGS AND SPECIFICATIONS ARE STUDENT WORK AND THE PROPERTY OF THE DESIGNER. AS SUCH, THEY ARE NOT INTENDED FOR USE ON OTHER PROJECTS OR EXTENSIONS OF THE SPECIFIED PROJECT WHATSOEVER.

OWNERSHIP: ALL DRAWINGS, SPECIFICATIONS, DESIGNS & COPIES THEROF ARE THE PROPERTY OF THE DESIGNER AND THE OWNER, WHETHER OR NOT THE WORK FOR WHICH THEY ARE MADE IS PERFORMED, AND ARE NOT TO BE USED OR DUPLICATED ON OTHER WORK EXCEPT BY WRITTEN CONSENT FROM THE DESIGNER AND OWNER.

REV	DESCRIPTION	DATE

PROJECT: PROJECT MODUNEST

ADDRESS: 109 BROCK ST. BARRIE, ON L4N 2M3

DRAWING: WALL DETAILS

SHEET: ID-3

DESIGNED BY: Taylor Giles

ISSUE DATE: 12/04/25


COURSE: INDE3001

SCALE: As indicated

2025-12-03 11:40:28 PM

DOOR SCHEDULE			
TAG	DESCRIPTION	MATERIAL	FRAME MATERIAL
101	SINGLE GLASS DOOR	GLASS	STEEL
102	SINGLE GLASS DOOR	GLASS	STEEL
103	DOUBLE DOOR GLASS: 68" x 84"	GLASS	STEEL
104	DOUBLE DOOR GLASS: 68" x 84"	GLASS	STEEL
105	INTERIOR SINGLE DOOR	WOOD	STEEL
106	INTERIOR SINGLE DOOR	WOOD	STEEL
107	DOUBLE DOOR GLASS: 68" x 84"	GLASS	STEEL
108	DOUBLE DOOR GLASS: 68" x 84"	GLASS	STEEL
109	DOUBLE DOOR GLASS	GLASS	STEEL
110	DOUBLE DOOR GLASS	GLASS	STEEL
111	INTERIOR SINGLE DOOR: 910x2110	WOOD	STEEL
112	INTERIOR SINGLE DOOR: 910x2110	WOOD	STEEL
113	INTERIOR SINGLE DOOR: 910x2110	WOOD	STEEL
114	SINGLE FLUSH 30" x 80"	WOOD	STEEL
115	OVERHEAD ROLLING DOOR	STEEL	STEEL
116	SINGLE FLUSH 30" x 80"	WOOD	STEEL
117	SINGLE FLUSH 30" x 80"	WOOD	STEEL
118	SINGLE FLUSH 30" x 80"	WOOD	STEEL
119	SINGLE FLUSH 30" x 80"	WOOD	STEEL
120	SINGLE FLUSH 30" x 80"	WOOD	STEEL
121	SINGLE FLUSH 30" x 80"	WOOD	STEEL

GRAND TOTAL: 21

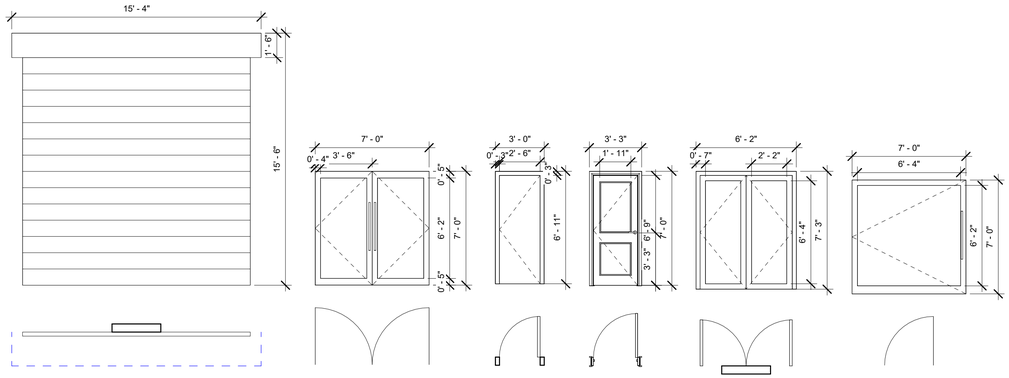

OVERHEAD ROLLING DOOR
168" x 168"

CURTAIN WALL DOUBLE DOORS
69" x 92"

SINGLE FLUSH
30" x 80"

SINGLE DOOR W/ TRANSOME
35" x 83"


DOUBLE GLASS DOORS
68" x 84"

CURTAIN WALL SINGLE DOOR
69" x 140"

DOOR LEGEND
1/4" = 1'-0"

WINDOW SCHEDULE						
TAG	TYPE	FRAME COLOUR	FRAME TYPE	SIZE	OPERATION	COUNT
W1	DOUBLE SLIDING	BLACK		72" x 60"	SLIDING	15

GRAND TOTAL: 15

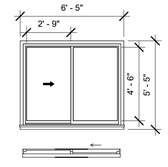

DOUBLE SLIDING WINDOW
72" x 60"

WINDOW LEGEND
1/4" = 1'-0"

TAYLOR DESIGNS

GILES.TAYLOR@YAHOO.COM - (705) 826-4206
1 GEORGIAN DR. BARRIE, ON

GENERAL NOTES:

1. THE CONTRACTOR AND ALL SUB-CONTRACTORS SHALL VERIFY ALL DIMENSIONS, DETAILS AND SPECIFICATIONS ON SITE AND REPORT ALL DISCREPANCIES IN WRITING TO THE DESIGNER BEFORE PROCEEDING WITH THE WORK.
2. DRAWINGS ARE NOT TO BE SCALED.
3. THE CONTRACTOR AND SUB-CONTRACTORS, BEFORE PROCEEDING WITH THE WORK, MUST SUBMIT ALL NECESSARY SAMPLES AND SHOP DRAWINGS TO THE DESIGNER FOR APPROVAL.
4. ALL CONCEPTS, DESIGNS, DETAILS, DRAWINGS AND SPECIFICATIONS ARE STUDENT WORK AND THE PROPERTY OF THE DESIGNER. AS SUCH, THEY ARE NOT INTENDED FOR USE ON OTHER PROJECTS OR EXTENSIONS OF THE SPECIFIED PROJECT WHATSOEVER.

OWNERSHIP: ALL DRAWINGS, SPECIFICATIONS, DESIGNS & COPIES THEROF ARE THE PROPERTY OF THE DESIGNER AND THE OWNER, WHETHER OR NOT THE WORK FOR WHICH THEY ARE MADE IS PERFORMED, AND ARE NOT TO BE USED OR DUPLICATED ON OTHER WORK EXCEPT BY WRITTEN CONSENT FROM THE DESIGNER AND OWNER.

REV	DESCRIPTION	DATE

PROJECT: PROJECT MODUNEST

ADDRESS: 109 BROCK ST. BARRIE, ON L4N 2M3

DRAWING: DOOR AND WINDOW SCHEDULE

SHEET: ID-4

DESIGNED BY: Taylor Giles

ISSUE DATE: 12/04/25

COURSE: INDE3001

SCALE: 1/4" = 1'-0"

2025-12-03 11:40:28 PM